PIANTA FABBRICATI E LOCALI - TONNARA DEL TONO - MILAZZO

Marzo 2015

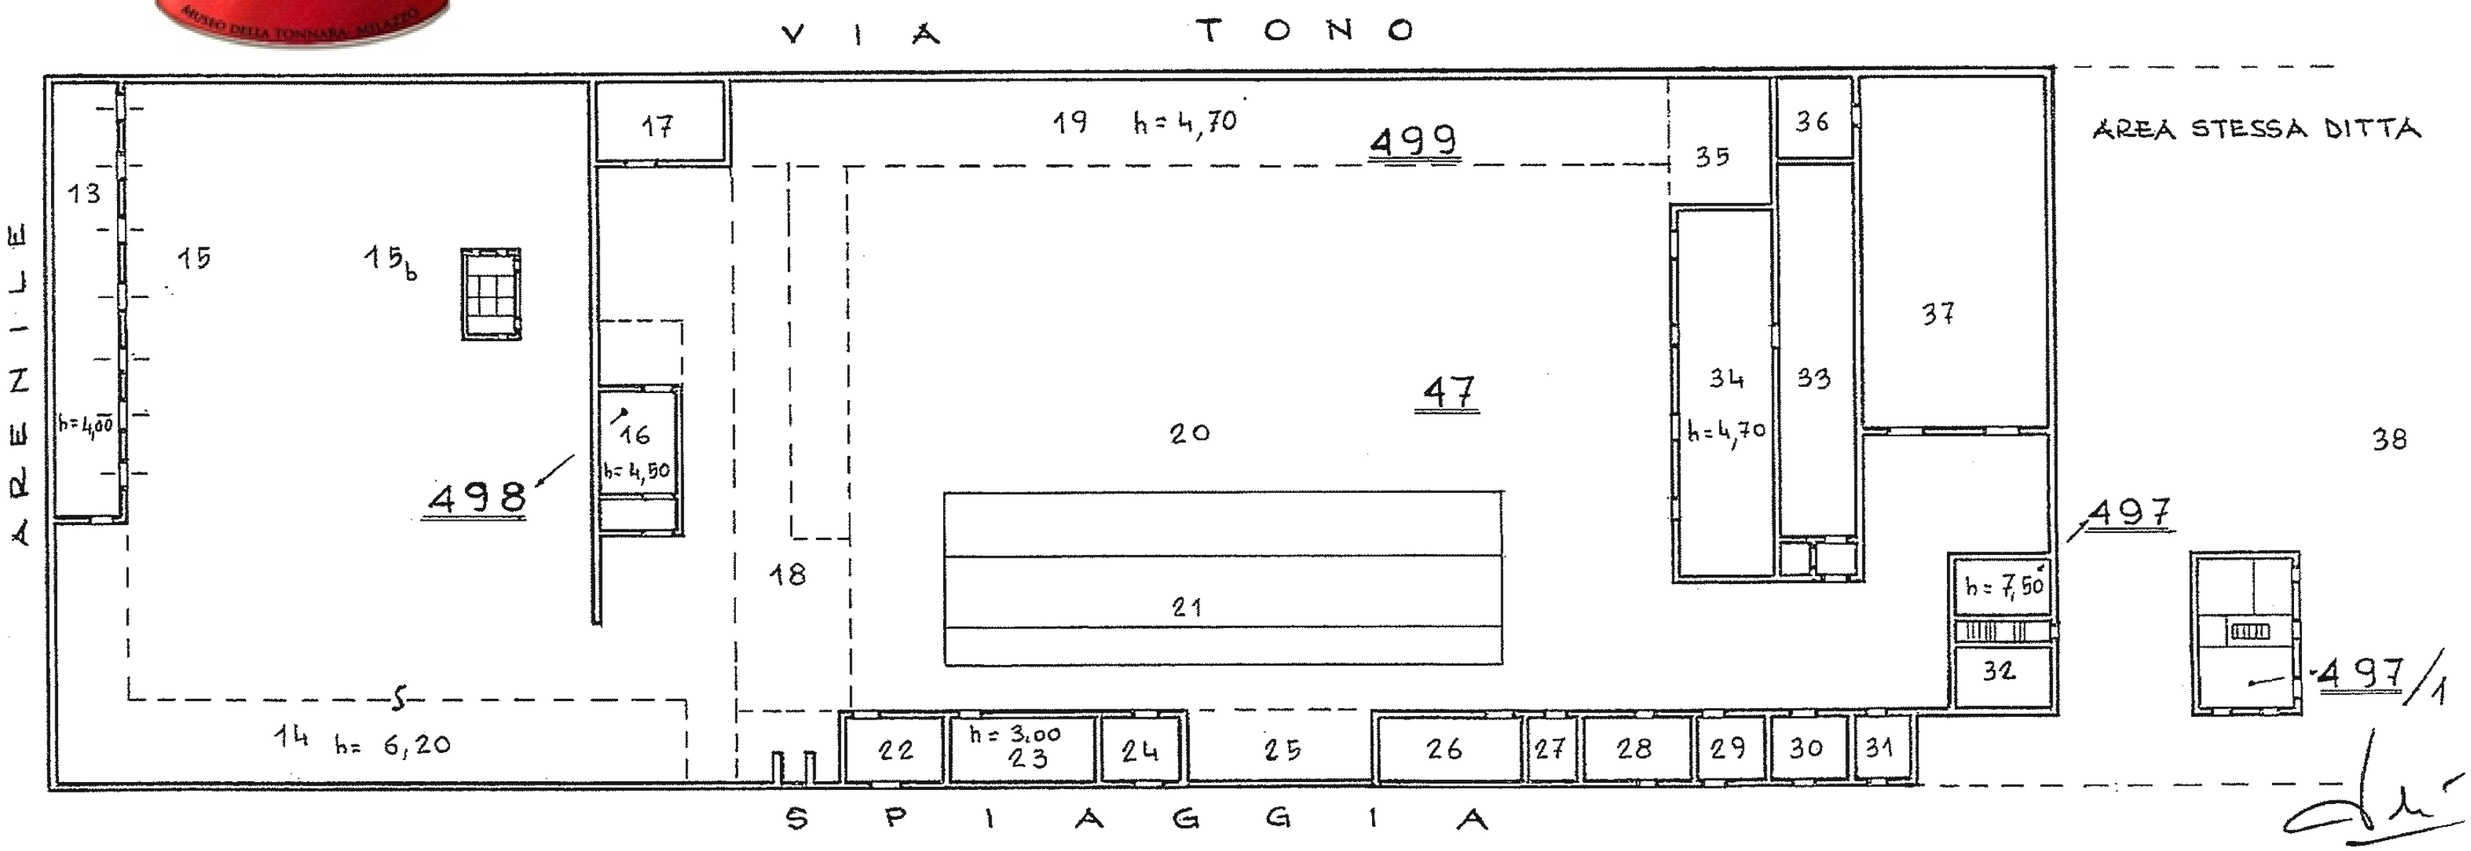

MILAZZO *a penna biro*

FOGLIO N. 4 - PART. N. 47 - 497 - 498 -499

N.B.: NEL FOGLIO DI MAPPA N° 4 DEL COMUNE DI MILAZZO LA PART. N° 498 È ERRONEAMENTE INDICATA CON IL N° 408

13 Camparia - Lavorazione uova e ventre di tonno con la tecnica di pietre su piani col sale, eseguita da maestranze trapanesi.

14 Ricovero galleggianti; deposito legna; falegnameria; lavori eseguiti da maestri d'ascia e bottari.

15 Spazio per:
A) Ghiacciaia per tonni e pesci spada, dotata di gruppo elettronico e relativi accumulatori.
B) Torchio per produzione olio di pesce.
C) Vasche col sistema a zappino (combustibile tipo pellet) per il trattamento e la colorazione della culica, con acqua calda e aghi di pino.

16 probabile locale pesa e punto vendita.

17 Guardiola.

18 Ingresso tonno pescato, trasporto su carrelli.

18 bis Sventratura, pulitura e impiccagione tonni, per vendita all'asta.

19 Affettatrice rotante.

20 Piazzale zona stipa per riempimento lattine di tonno.

21 Zona caldaie (n. 6 + 6) per bollitura pesci, alimentate a carbone e legna.

22 Uffici.

23. Zona riposo.

24. Locale muratori.

25 Deposito sale e pozzo con serbatoio collegato col mare.

26 Cucina per produzione Cincina in barili.

27 Deposito sale.

28 Locale officina fabbro ferraio per ancore e catene.

29 Locale meccanici.

30 Locale elettricisti.

31 Locale stagnini.

INGRESSO AREA n. 497

32 Locale direzione.

33 Locale Corpo di guardia.

34-36-37 Magazzini deposito contenitori di latte piene e vuote.

35 Locale deposito olio.

Per gentile concessione di Enzo Giuffrè